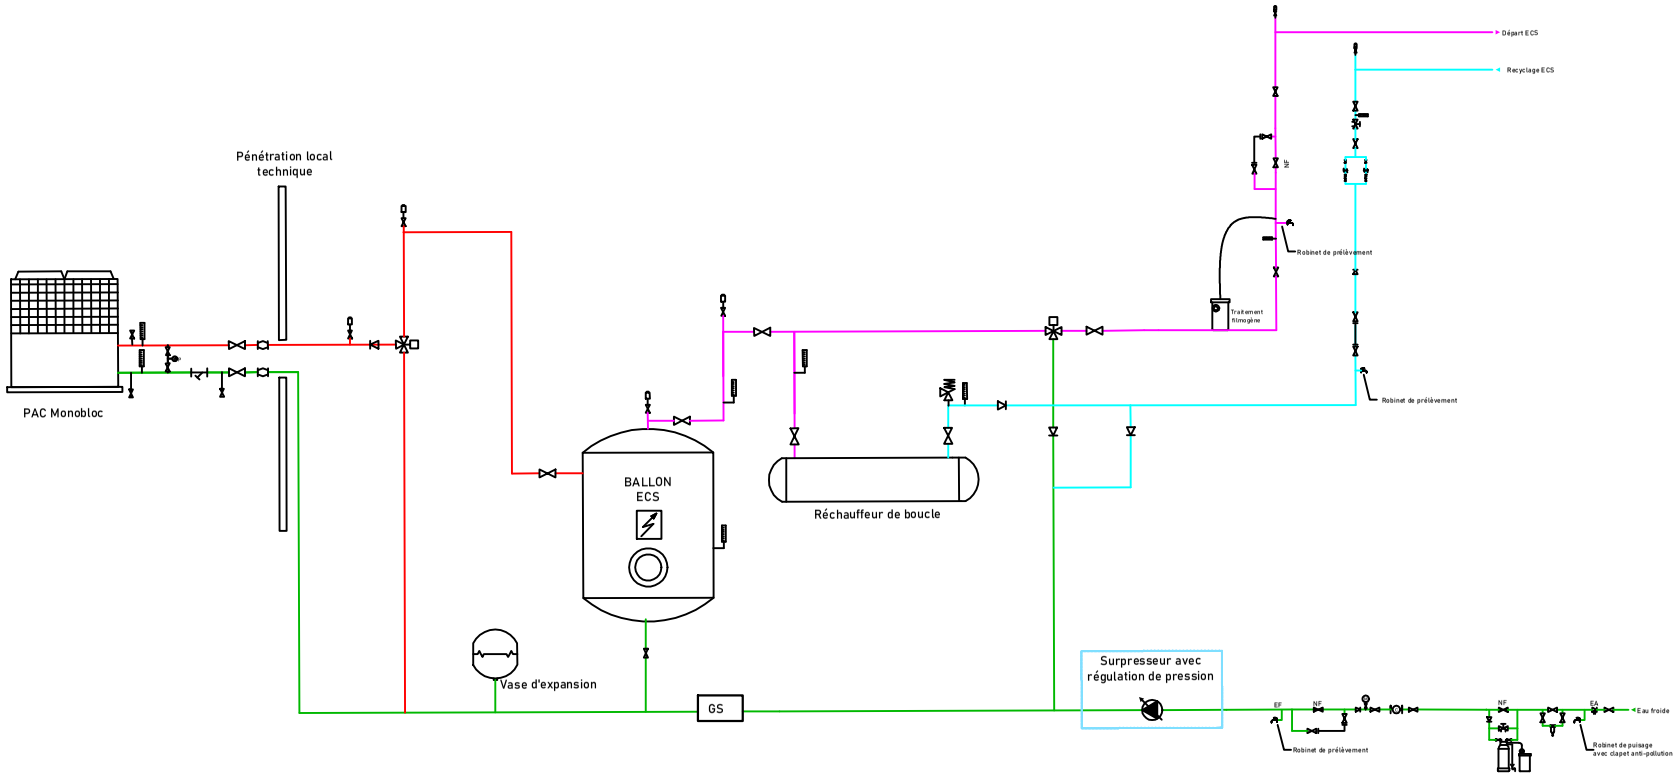


Maîtrise d'ouvrage	Bureau d'études	Descriptif du projet	Détails
HAUTS-DE-SEINE HABITAT	MANERGY	Rénovation production ECS - RPA Champs Philippe Schéma de principe projeté	Date : Avril 2025 Échelle : S0 Format : A4 Indice : 0