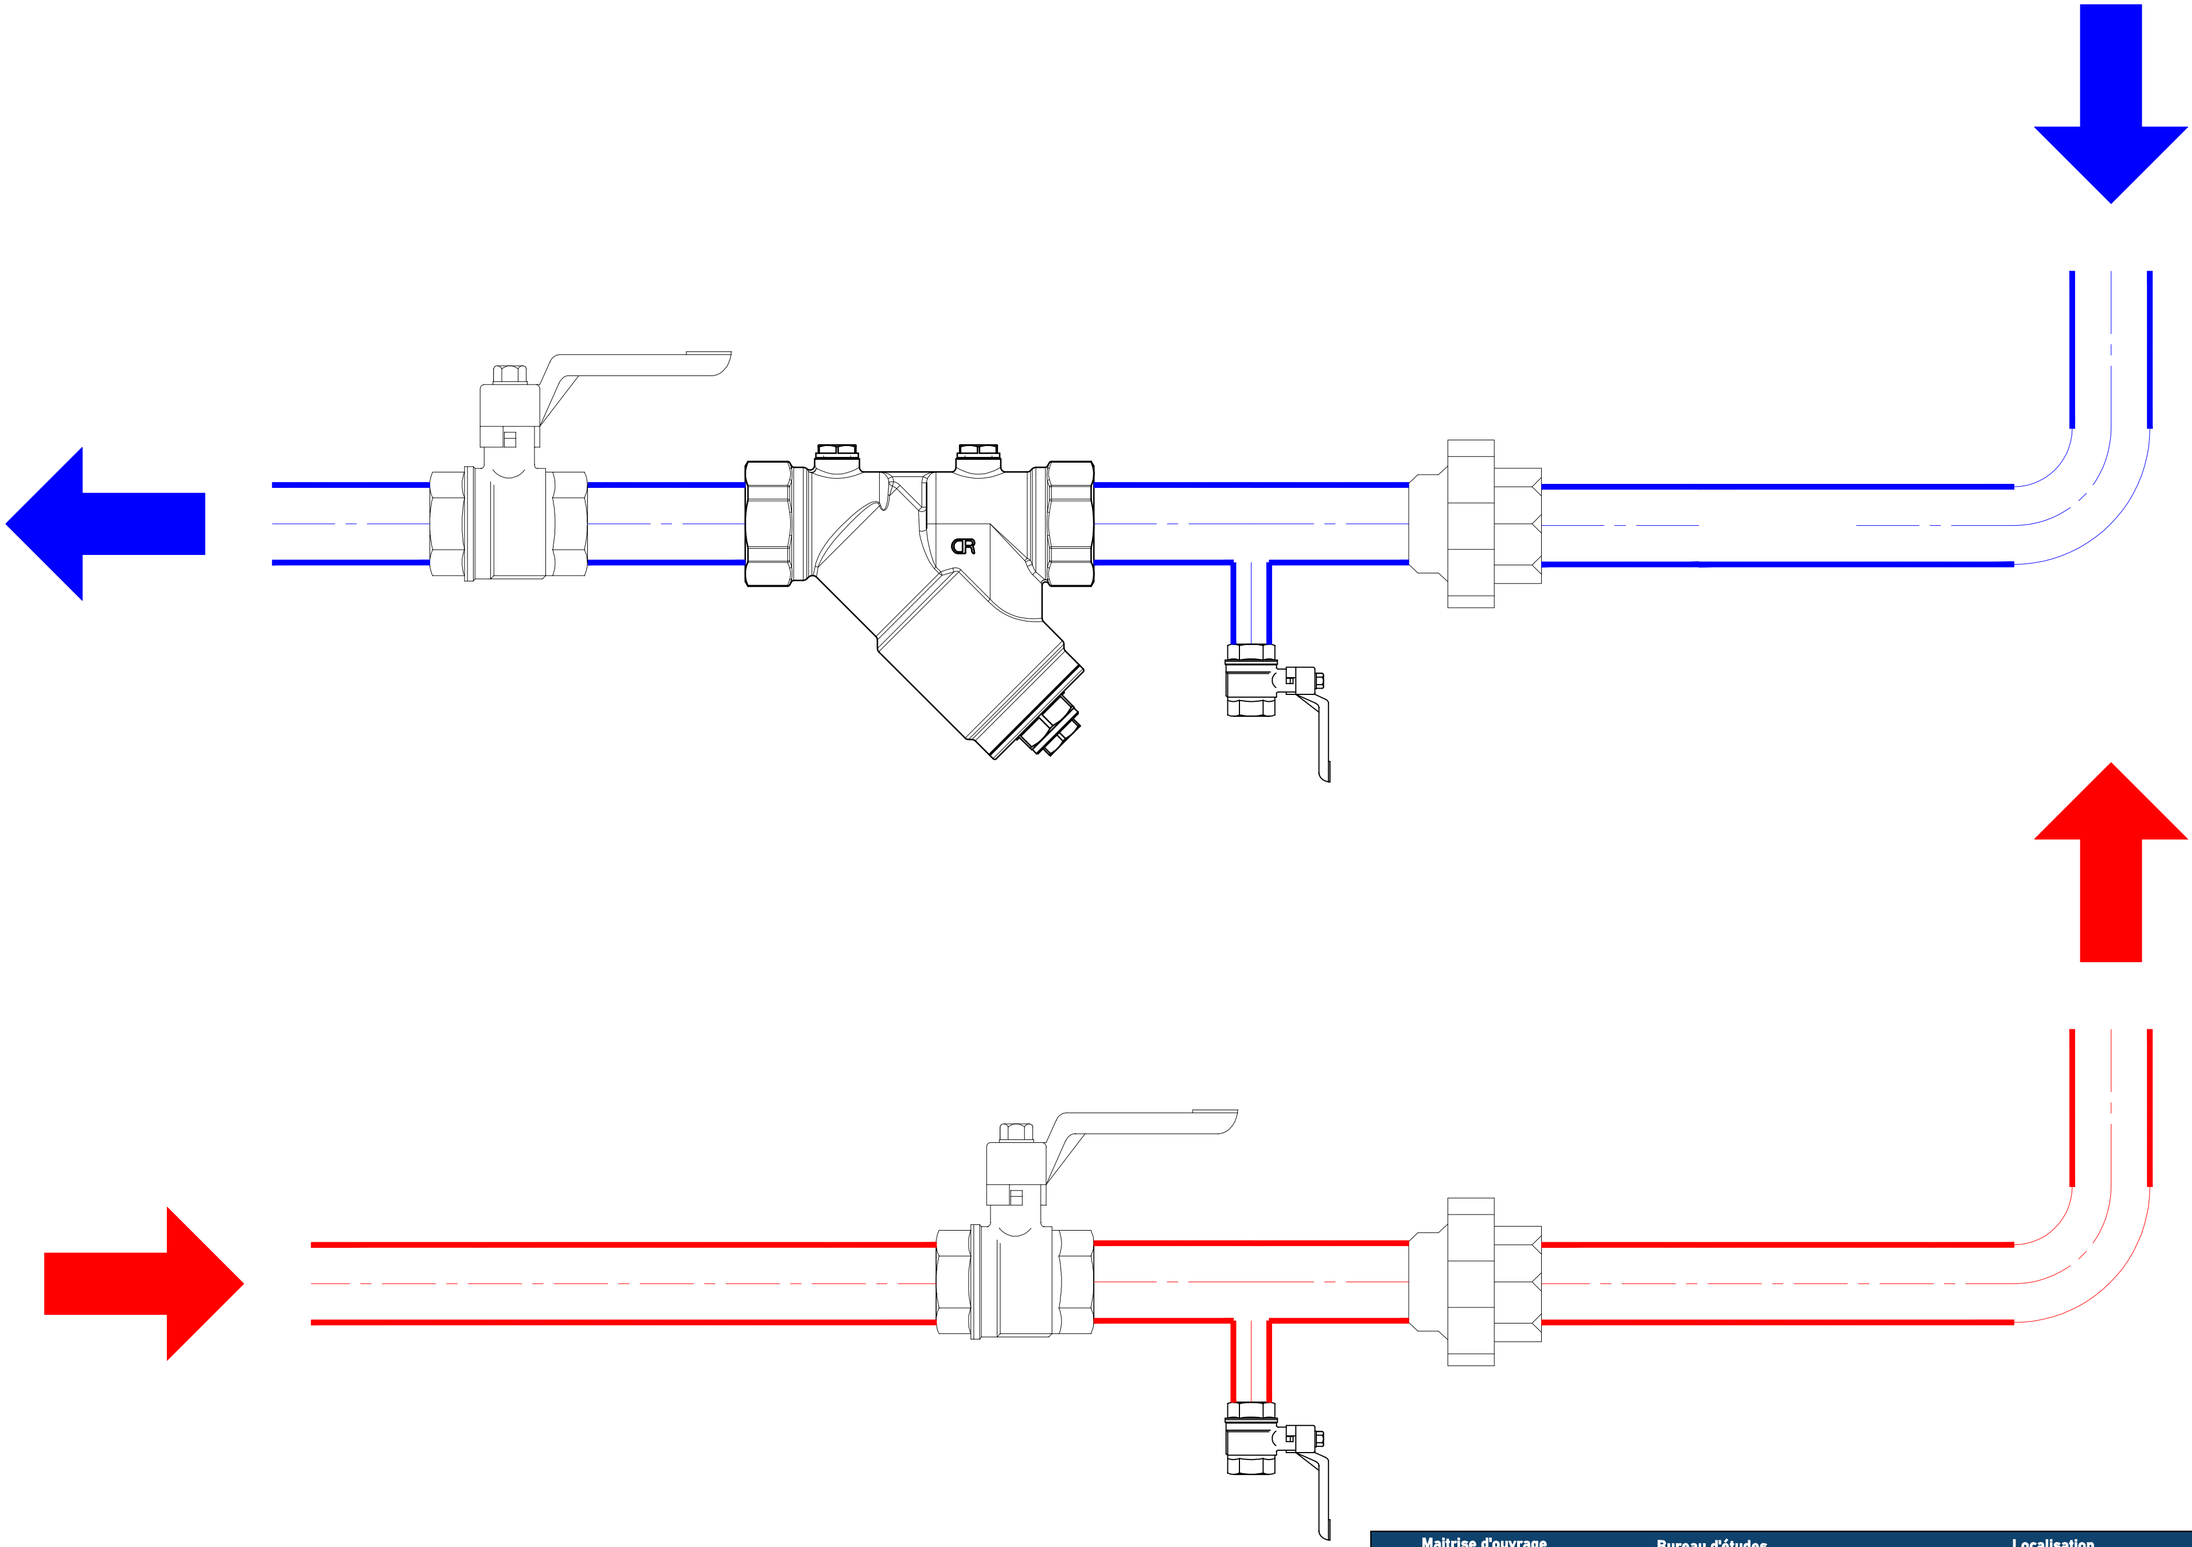


Maitrise d'ouvrage	Bureau d'études	Localisation	Détails
HAUTS-DE-SEINE HABITAT	MANERGY HABITAT & ÉQUIPEMENTS COLLECTIFS	RPA Champs Philippe SCHEMA HYDRAULIQUE PdC ECS	Date : Décembre 25 Format : A2 Échelle : ## Plan : N° 1